


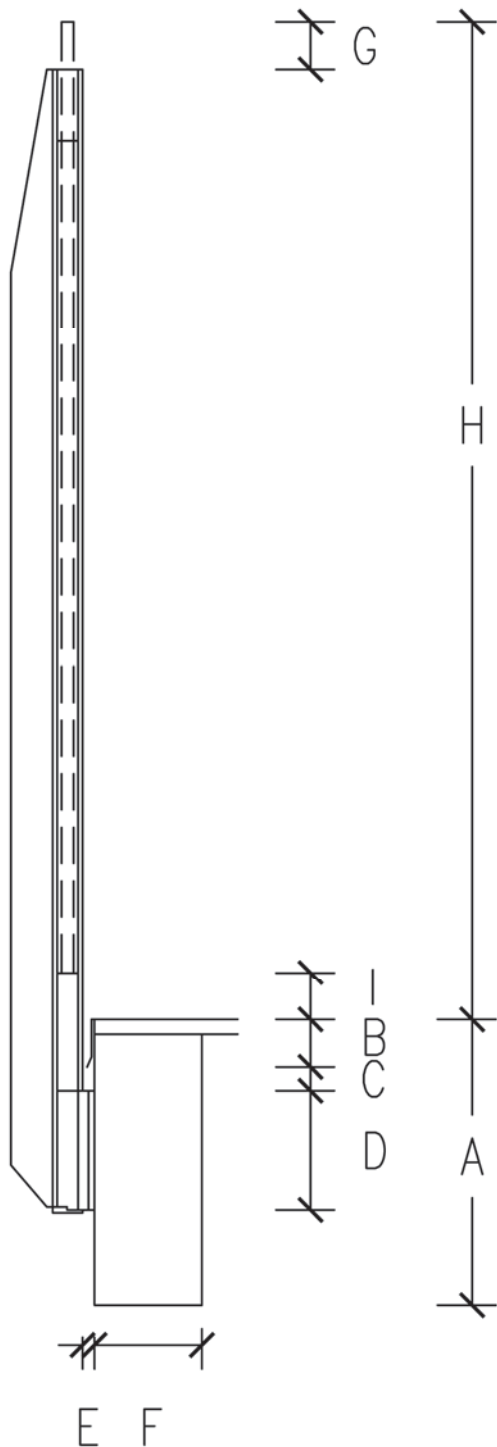

- A: _____ FASCIA HEIGHT INCLUDING DECKING
- B: _____ DRIP EDGE, NOSING OR FLASHING
- C: _____ GAP FROM B TO TOP OF BASE PLATE
- D: _____ BASE HEIGHT PLATE IF NOT STANDARD*
- E: _____ OFFSET IF NOT STANDARD*
- F: _____ BLOCKING DEPTH AT FASCIA** (MIN. 4.5")
- G: _____ GLASS EXTENSION ABOVE POST (2" TYP.)
- H: _____ RAIL HEIGHT AT GLASS FROM DECK
- I: _____ GAP BELOW GLASS TO DECK (2" TYP.)

HOLE SIZE**
(FOR FASTENERS)

*** NOTE:**
STANDARD BASE PLATE HEIGHT IS 5" AND STANDARD
OFFSET IS 7/16", EXTENDED OFFSET IS 1 1/2"

**** IMPORTANT:**
PLEASE ENSURE TOPLESS RAIL ALONG WITH
FASTENING DETAILS ARE ACCEPTABLE TO LOCAL
BUILDING AUTHORITIES. UNLESS STATED OTHERWISE
ON PROPOSALS/SALES ORDERS SITE SPECIFIC
ENGINEERING IS NOT INCLUDED.

***** NOTE:**
GLASS IS NOT INCLUDED WITH THE INFINITY SYSTEM

THIS DRAWING IS FOR MATERIAL ESTIMATION AND LAYOUT
CLARIFICATION PURPOSES ONLY. PLEASE ENSURE THAT THE FINAL
SALES ORDER IS CHECKED THOROUGHLY FOR ACCURACY.